
二级表安装定位总图

依据最新 NET 描述编制 · 二级表位置、北侧入口开挖位置及待选位置

96 个节点 / 94 条管段 / 管长 1,905.821 m

10 处描述标注：9 个节点 + 1 个管段

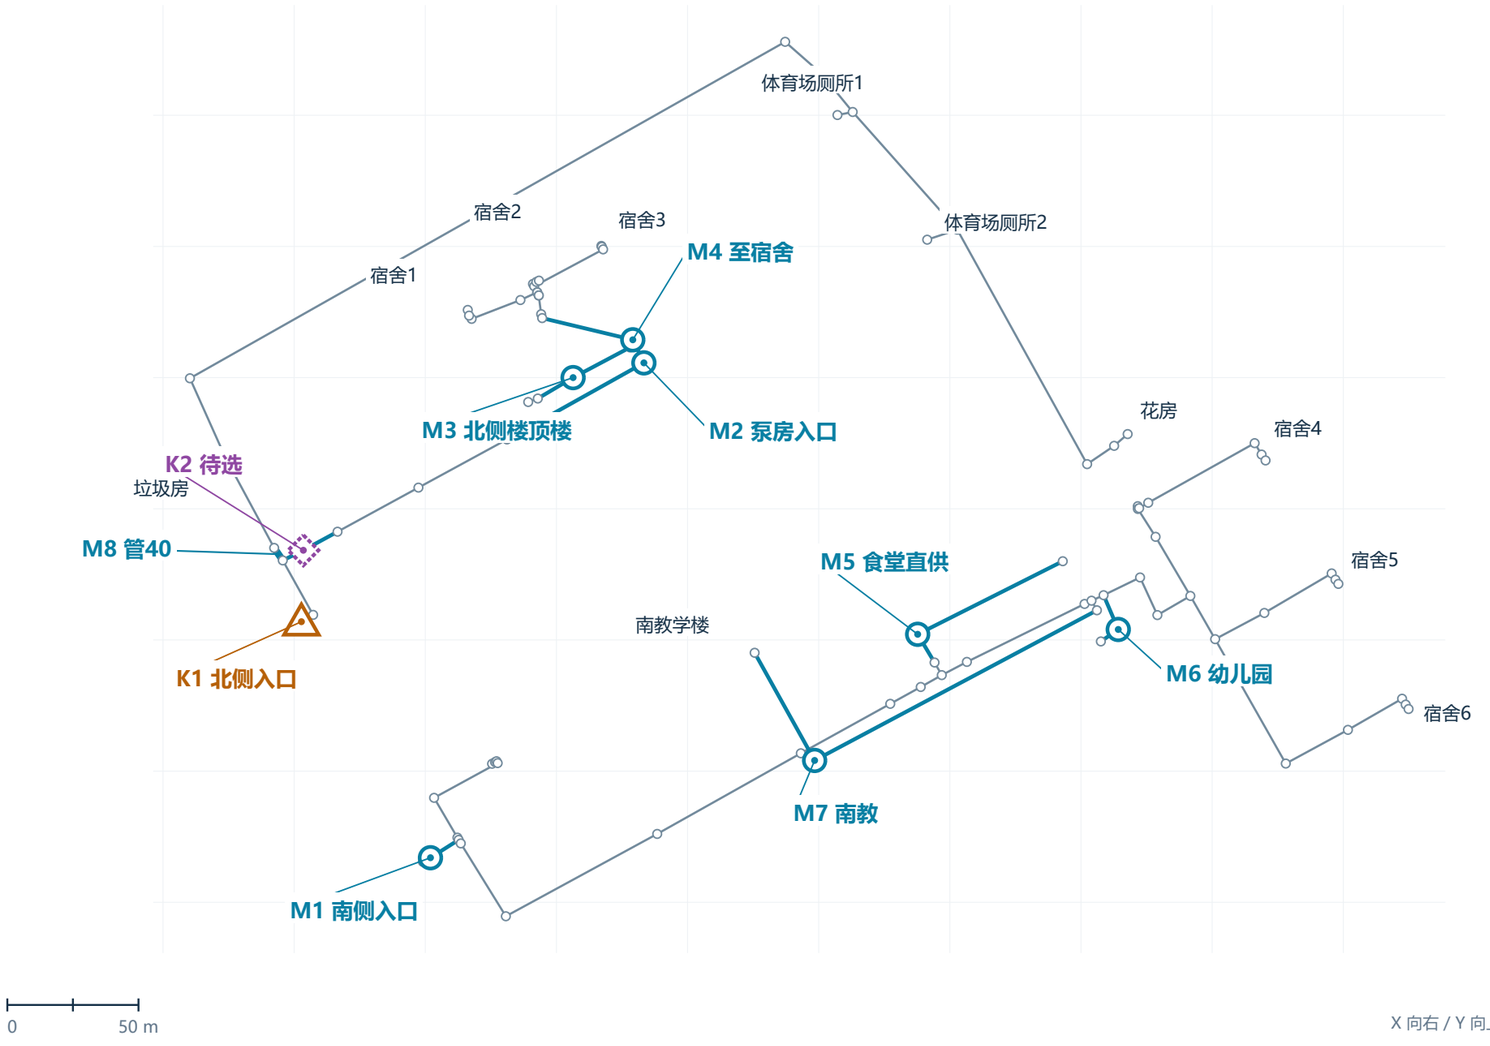

X 向右 / Y 向上；方位未核实

图例与读图

- 二级表标注
- 开挖位置
- 开挖待选位置
- 管段二级表标注（整段）
- 最新文件管线

图册 K1/K2、M1-M8 为定位索引；核对时使用原始节点或管段 ID。M8 对应整条管40，源文件未给出段内精确安装点。两处北侧开挖标注不自动等于两台设备。

使用范围

用于踏勘定位、安装点确认和交接。相邻管径为管道参数，不能直接作为水表口径或采购数量。开挖范围、最终安装位置与设备规格须现场确认。

源文件状态

最新文件为 96 个连接节点、94 条管线，无水库、水箱或泵链接；文件未给出水力流向。图中不沿用旧版水源符号。

坐标按源文件数值绘制，单位 m；坐标系和现场基准未给出。所有线条均可在 PDF 中放大查看。

编制依据 campus_water_completed1026_管长_铸铁DN200.net

源文件 SHA-256：ac8c23b1d996ce80c667dfa225e4b4b57c7104c86e29d18629e258e0a40f7503

原文件标题仍含 2026-10-13 与旧统计；本图册以实际解析的 2026-10-26 文件内容为准。

安装点位与原始描述清单

原始中文描述逐项保留；坐标四舍五入至 0.001 m；完整精度保留在源文件及系统数据中

图册号 / 节点	位置类别	源文件原始描述	源 X / 源 Y (m)	相邻管段原编号	详图页
K1 / JS643	开挖位置	开挖二级表，北侧入口	-16747.231 -7743.044	L004, L005	03
K2 / JS258	开挖待选	开挖二级表-北侧入口待选	-16746.500 -7715.815	L006, L007	03
M1 / JS54	二级表标注	二级表-南测入口	-16698.023 -7833.014	L014, L015	05
M2 / JS238	二级表标注	二级表-北侧泵房入口	-16616.653 -7644.381	17, 18	04
M3 / 19	二级表标注	二级表-北侧楼顶楼	-16643.643 -7649.998	20, 23	04
M4 / 21	二级表标注	北侧泵房-to宿舍 二级表	-16620.883 -7635.586	24, 25	04
M5 / JS70	二级表标注	二级表-食堂直供	-16512.272 -7747.843	L085, 4	06
M6 / 7	二级表标注	二级表-幼儿园	-16435.785 -7746.005	32, 33	06
M7 / 27	二级表标注	南教 二级表	-16551.556 -7795.933	38, 39	06
M8 / 管40	管段二级表标注	二级表-垃圾房+体育管+花房	两端坐标见第03页	管40: JS641 - 28	03

数量与名称的判读

共检出 10 处“二级表”描述：7 个普通节点、2 个开挖相关节点及1条管段。JS258 明确标为“待选”；源文件未说明其与 JS643 的最终取舍关系，不能自行认定二选一或同时安装。


JS54 原文“南测入口”在定位图中按“南侧入口”展示；节点19的“北侧楼顶楼”、管40的“体育管”均保留原文。具体位置名称、楼栋与安装高度待现场确认。

所有列出的相邻管线在文件中均为 DN200、铸铁管；部分管径为源文件默认补全值，管长为模型记录值。设备口径、安装形式、直管段要求和附件清单应结合现场及最终选型确认。

以节点 ID 找点，再沿相邻管段核对连接关系；线条交叉但未共用节点时，不认定为管线连通。图册不把图上的端点顺序作为水流方向。

北侧入口及垃圾房等支路计量位置

K1 / JS643 开挖 · K2 / JS258 开挖待选 · M8 / 管40 垃圾房+体育管+花房

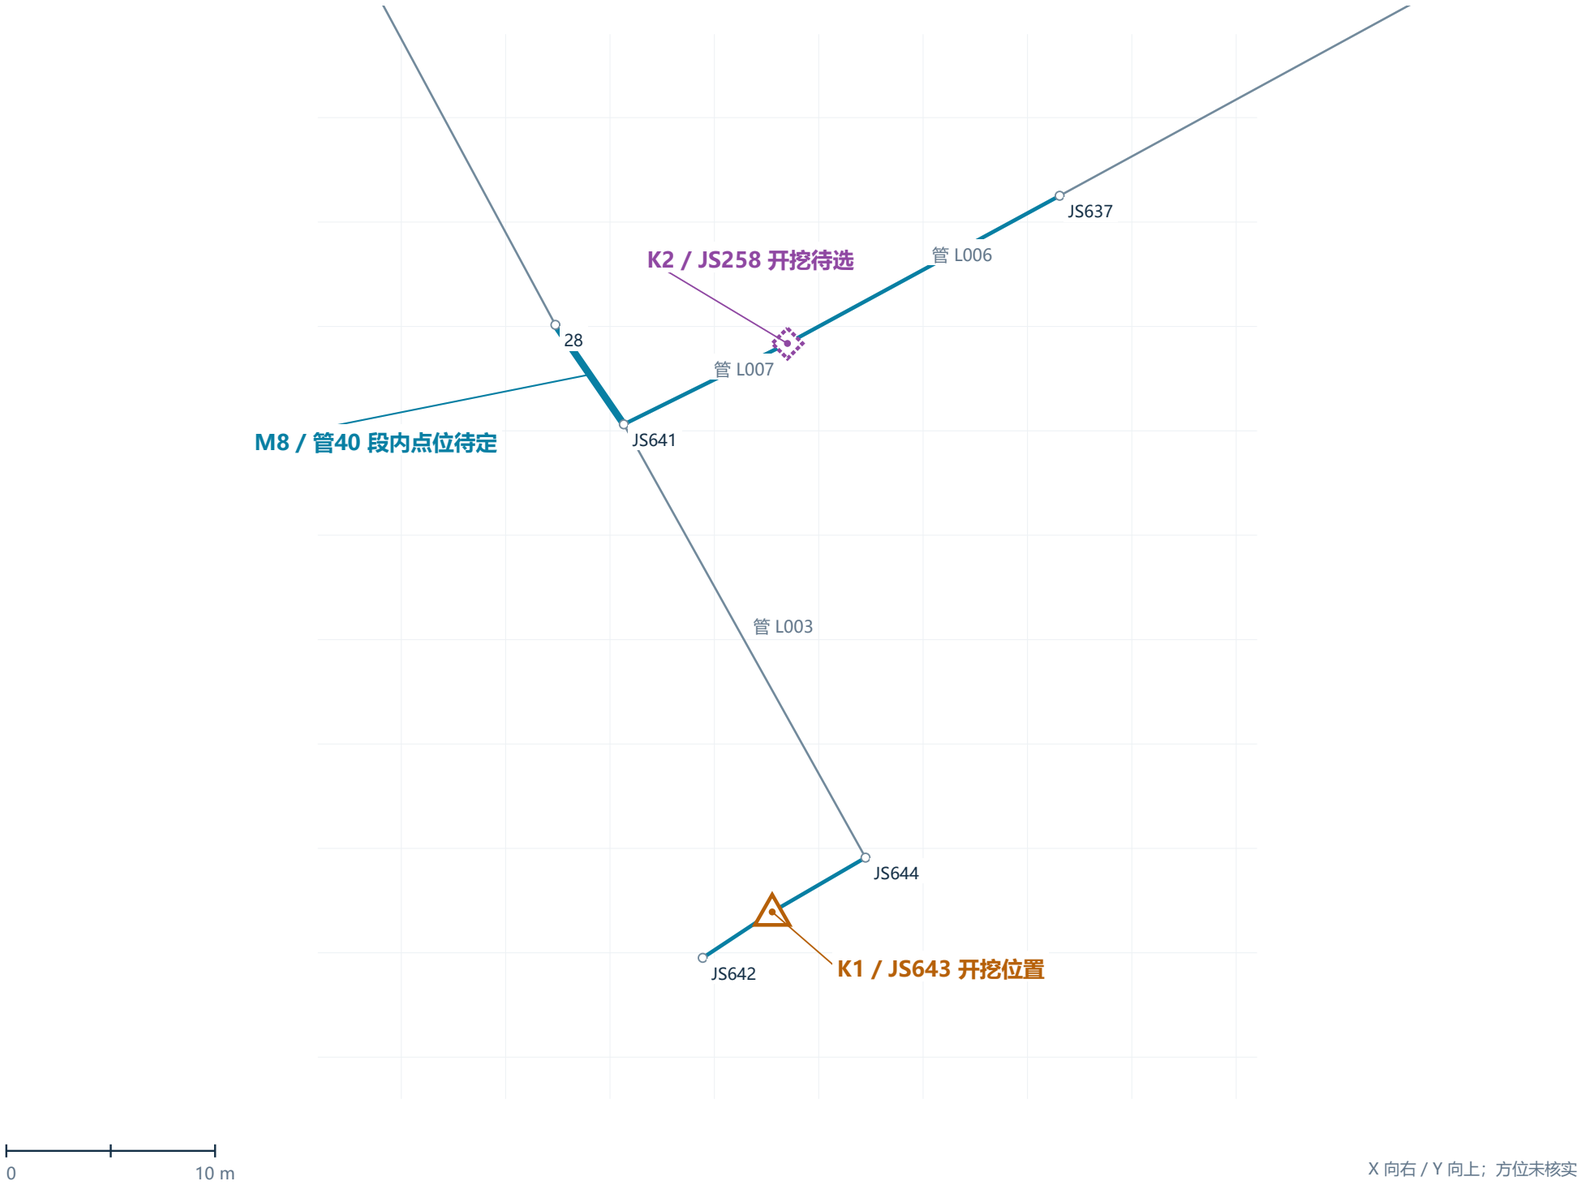

K1 北侧入口

节点 JS643

源描述：开挖二级表，北侧入口

源 X -16747.231 / 源 Y -7743.044

相邻管线（端点顺序不代表供水方向）

L004: JS643 - JS642

DN200 / 铸铁管 / 3.989 m

L005: JS643 - JS644

DN200 / 铸铁管 / 5.173 m

源标签 C01_WATER_METER；井室与可安装条件待核实。

K2 北侧入口待选

节点 JS258

源描述：开挖二级表-北侧入口待选

源 X -16746.500 / 源 Y -7715.815

相邻管线（端点顺序不代表供水方向）

L006: JS258 - JS637

DN200 / 铸铁管 / 14.836 m

L007: JS258 - JS641

DN200 / 铸铁管 / 8.743 m

源标签 C01_PIPE_POINT；描述明确“待选”，最终用途及取舍待现场确认。

M8 垃圾房+体育管+花房

二级表-垃圾房+体育管+花房 | 材质=铸铁管 MAT=CAST_IRON; DN200; 管长按坐标计算(米)

管40: JS641 - 28 / DN200 / 5.784 m

JS641: X -16754.338 / Y -7719.689

28: X -16757.616 / Y -7714.924

图上加粗整段，指引线只用于标注，不代表段内精确安装点。


K1 与 K2 平面直线间距 27.24 m；只用于区分位置，不是开挖长度或沿管距离。

现场确认：最终选点 _____ 计量范围 _____ 开挖范围 _____ 现场负责人 / 日期 _____

定位顺序：原始节点 ID → 相邻井点与管段 → 现场管径及埋设位置 → 最终安装点签认。

北侧泵房与教学楼支路

M2 / JS238 泵房入口 · M3 / 19 北侧楼顶楼 · M4 / 21 泵房至宿舍

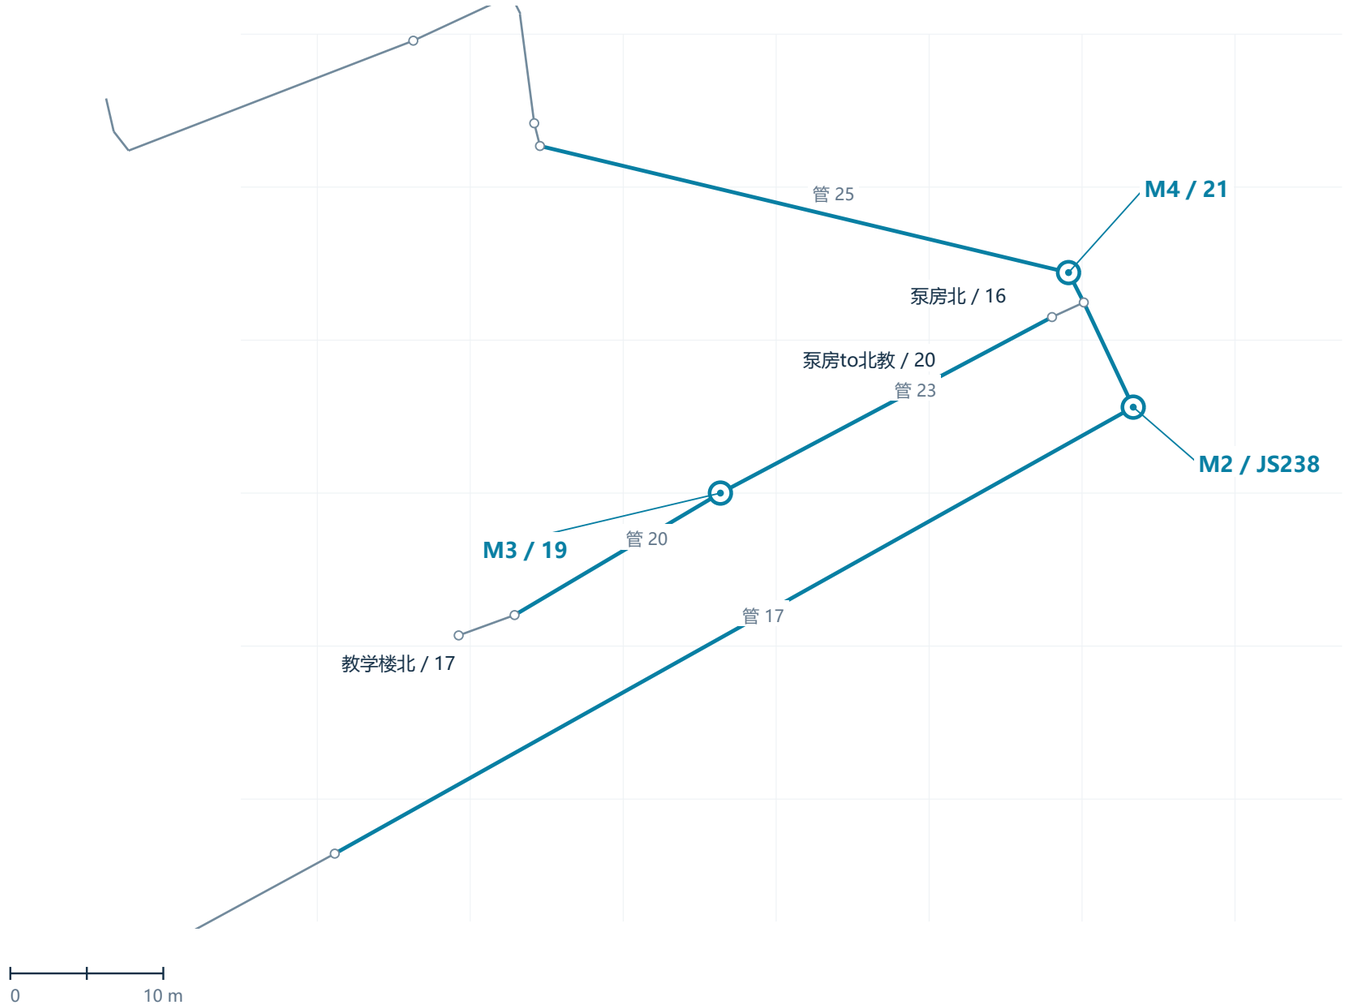

M2 北侧泵房入口

节点 JS238

源描述：二级表-北侧泵房入口
源 X -16616.653 / 源 Y -7644.381

相邻管线（端点顺序不代表供水方向）

17: JS238 - JS239
DN200 / 铸铁管 / 59.809 m

18: 16 - JS238
DN200 / 铸铁管 / 7.568 m

相邻管17、18的 DN200 在源描述中为默认补全值，须现场核实。

M3 北侧楼顶楼

节点 19

源描述：二级表-北侧楼顶楼
源 X -16643.643 / 源 Y -7649.998

相邻管线（端点顺序不代表供水方向）

20: 19 - 18
DN200 / 铸铁管 / 15.643 m

23: 20 - 19
DN200 / 铸铁管 / 24.544 m

“北侧楼顶楼”为源描述；具体楼栋及安装高度未给出。

M4 北侧泵房至宿舍

节点 21

源描述：北侧泵房-to宿舍 二级表
源 X -16620.883 / 源 Y -7635.586

相邻管线（端点顺序不代表供水方向）

24: 16 - 21
DN200 / 铸铁管 / 2.192 m

25: JS208 - 21
DN200 / 铸铁管 / 35.534 m

源标签为“泵房to宿舍”；与泵房节点16由管24连接。


泵房邻近节点核对

M2 为 JS238，M4 为 21，两者不是泵房节点16本身。M3 为节点19，位于节点20与18之间；不要与管段编号19混淆。图中“管”前缀表示管段 ID。

模型记录管24长 2.192 m（16 - 21），管18长 7.568 m（16 - JS238）；这些是相邻整段管长，不代表设备安装预留长度。


南侧入口：二级表节点 JS54

M1 / JS54 · 源描述“二级表-南测入口” · 入口处多个井点相距较近，按 ID 精确区分

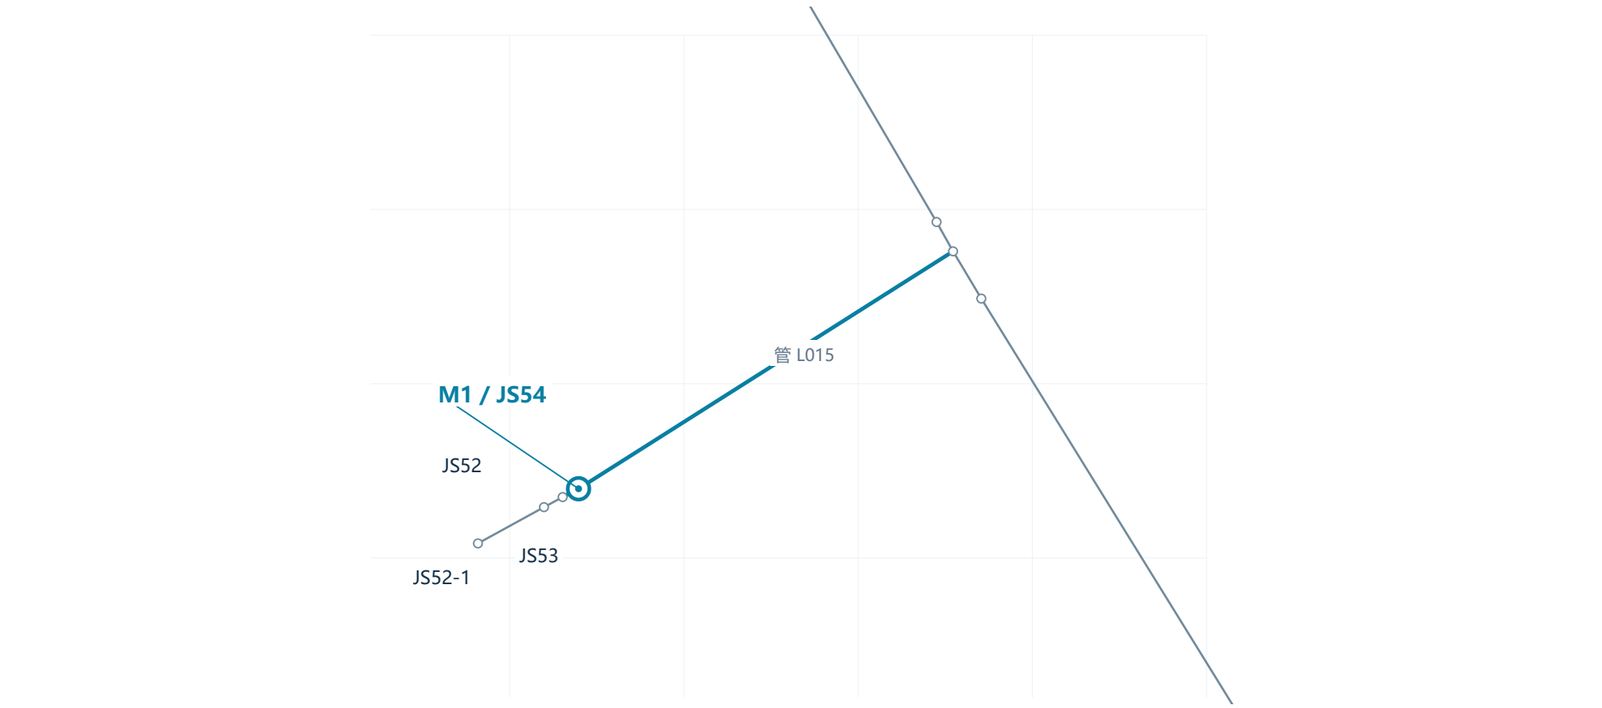

X 向右 / Y 向上；方位未核实

入口近距放大

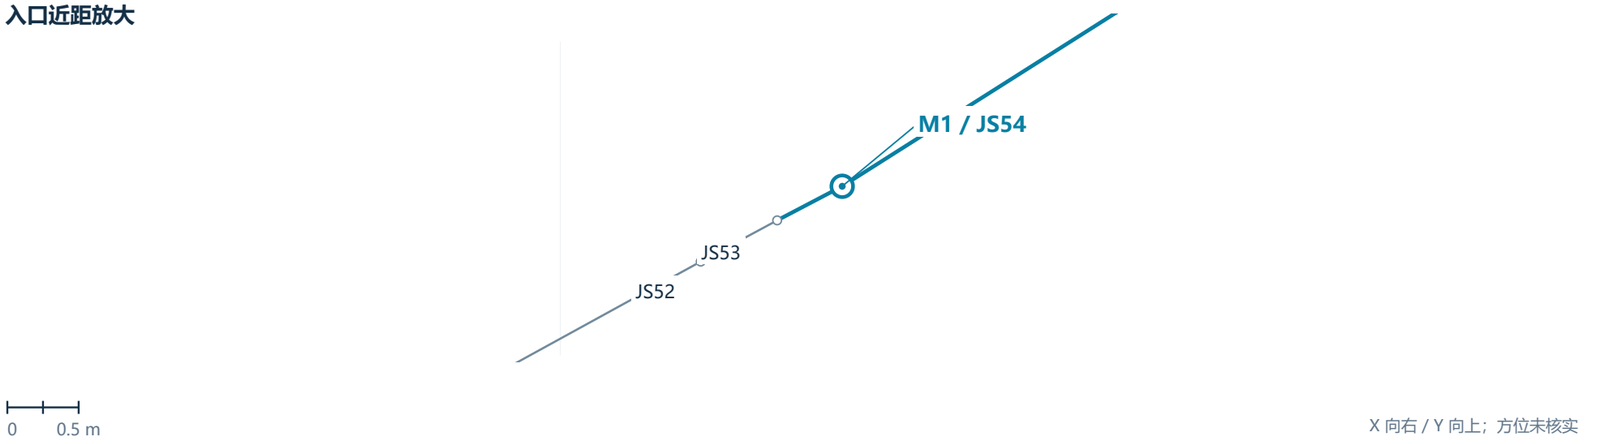

X 向右 / Y 向上；方位未核实

M1 南侧入口

节点 JS54

源描述：二级表-南测入口

源 X -16698.023 / 源 Y -7833.014

相邻管线（端点顺序不代表供水方向）

L014: JS53 - JS54

DN200 / 铸铁管 / 0.515 m

L015: JS54 - JS55

DN200 / 铸铁管 / 12.724 m

源标签为 C01_VALVE_ACCESS。保留原始设施类型和二级表描述，不能仅凭“阀门孔”标签假定井室已具备安装条件。


现场核对重点

JS54 与相邻 JS53 之间的管 L014 记录长约 0.515 m，属于不同节点。请核对入口实际管线、可用安装空间及对应井点，避免把二级表装在邻近错误节点。

最新源文件中 JS52-1 的节点类别为连接节点；图册依源文件绘制。仅凭其位于入口附近，不将其标成已设置的水力水源。


食堂直供、幼儿园与南教学楼

M5 / JS70 食堂直供 · M6 / 7 幼儿园 · M7 / 27 南教

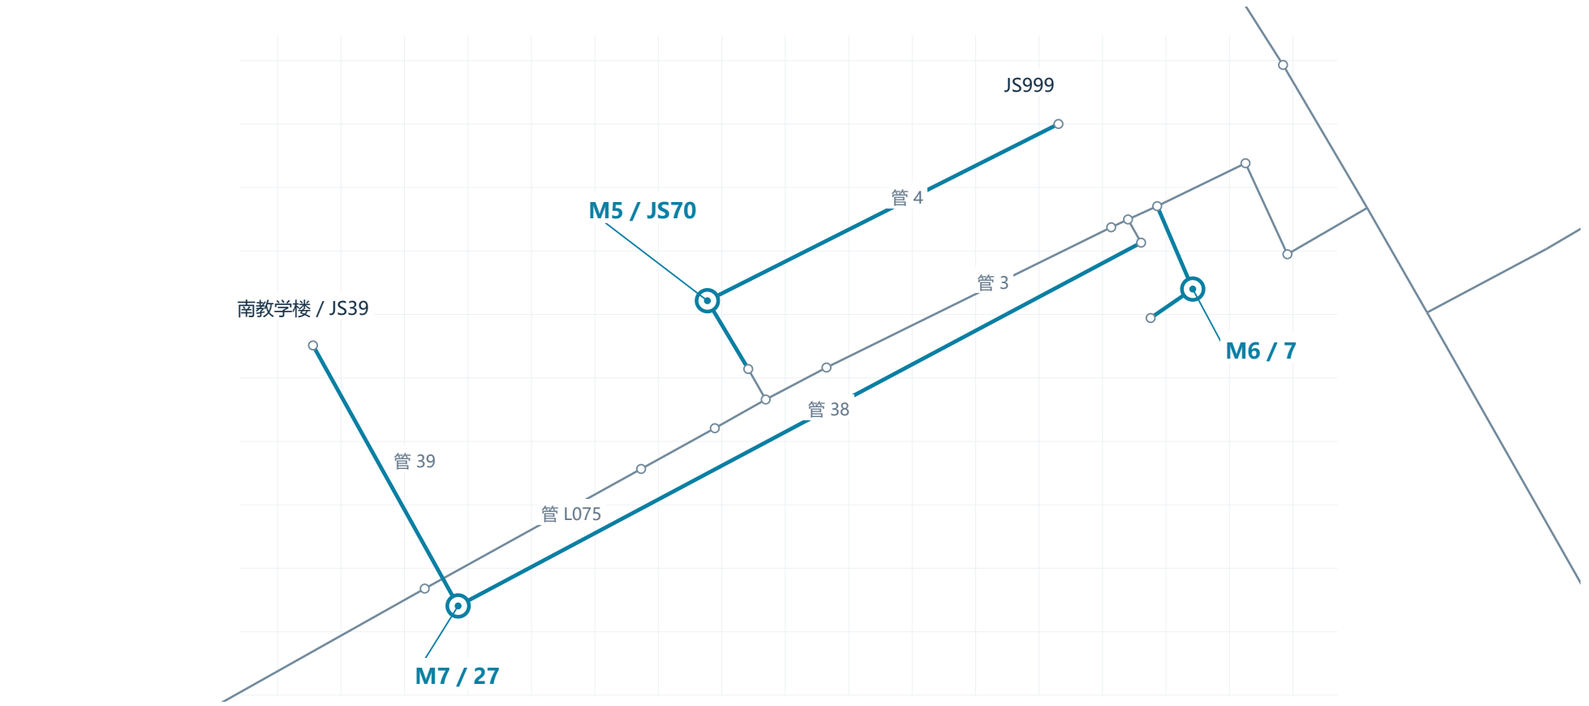

X 向右 / Y 向上；方位未核实

南泵房与幼儿园支路放大

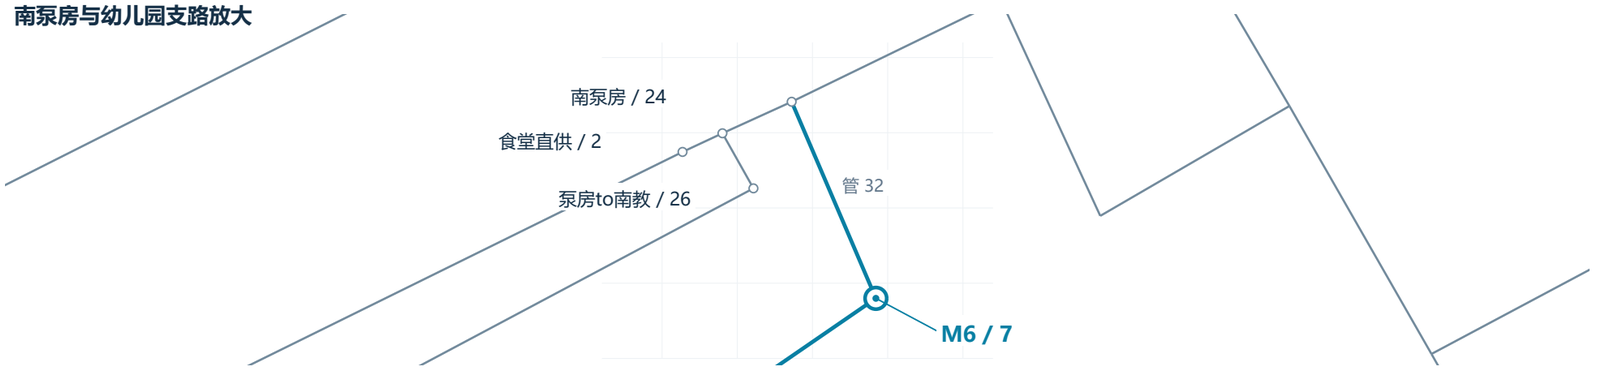

X 向右 / Y 向上；方位未核实

M5 食堂直供

节点 JS70

源描述：二级表-食堂直供

源 X -16512.272 / 源 Y -7747.843

相邻管线（端点顺序不代表供水方向）

L085: JS70 - JS69

DN200 / 铸铁管 / 12.539 m

4: JS70 - JS999

DN200 / 铸铁管 / 61.941 m

描述指向二级表节点 JS70；食堂直供用户节点2不是该二级表节点。

M6 幼儿园

节点 7

源描述：二级表-幼儿园

源 X -16435.785 / 源 Y -7746.005

相邻管线（端点顺序不代表供水方向）

32: 1 - 7

DN200 / 铸铁管 / 14.214 m

33: 25 - 7

DN200 / 铸铁管 / 8.053 m

描述为“二级表-幼儿园”，通过管32、33连接节点1和25。

M7 南教

节点 27

源描述：南教 二级表

源 X -16551.556 / 源 Y -7795.933

相邻管线（端点顺序不代表供水方向）

38: 26 - 27

DN200 / 铸铁管 / 121.904 m

39: JS39 - 27

DN200 / 铸铁管 / 46.985 m

节点27经管38接节点26（泵房to南教），经管39接南教学楼 JS39。

现场确认与安装交接记录

按原始节点 / 管段 ID 逐点记录；候选点及段内安装点完成签认后再计入安装数量

图册号 / 节点	位置	现场点位 / 计量范围确认	实测管径 / 最终表径	安装方式 / 附件	设备编号 / 照片编号	签认 / 日期
K1 / JS643	北侧入口					
K2 / JS258	北侧入口待选					
M1 / JS54	南侧入口					
M2 / JS238	北侧泵房入口					
M3 / 19	北侧楼顶楼					
M4 / 21	北侧泵房至宿舍					
M5 / JS70	食堂直供					
M6 / 7	幼儿园					
M7 / 27	南教					
M8 / 管40	垃圾房+体育管+花房					

本版交接需确认的事项

1. 北侧入口 K1 / K2：最终保留点及用途 _____；M8 管40段内精确安装点 _____。

2. M3“北侧楼顶楼”：具体楼栋 _____；楼层 / 高度 _____。M1“南测入口”名称核对 _____。

3. 每点安装后补录实际坐标、设备口径及编号、安装照片与现场连接关系，并回写系统；候选点是否取消需明确记录。

确认后的安装总数 _____ 台　　现场负责人 _____　　建设方确认 _____

数据版本：campus_water_completed1026_管长_铸铁DN200.net